
01

Steel and glazing

Survey, level the supports, convert the old door to W1, seal end B

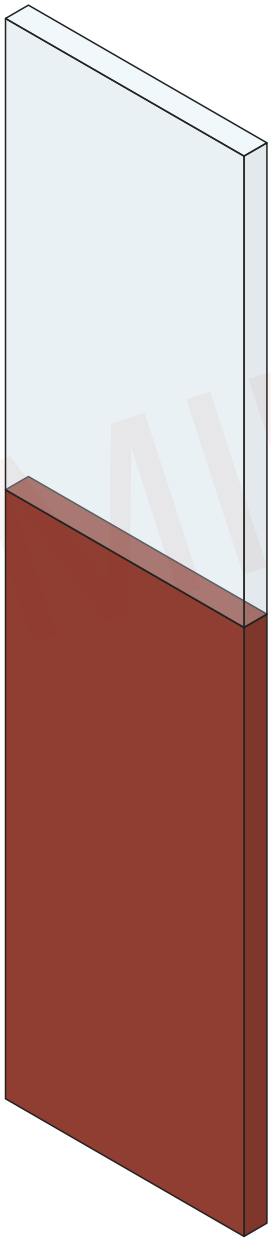

! Survey sheet first: nothing is cut before study/studio/survey.csv is complete.

PRELIMINARY

Farm container studios	farm.databayt.org/docs/studio
Survey, level the supports, convert the old door to W1, seal end B	AS-01
Scale NTS · Rev A · 2026-10-26 · mm	PRELIMINARY

02

Insulation and lining

Seal the floor, prime the steel, foam-fill the corrugation valleys



PRELIMINARY


! Epoxy floor seal: do not sand the treated floor.

Farm container studios	farm.databayt.org/docs/studio
Seal the floor, prime the steel, foam-fill the corrugation valleys	**AS-02**
Scale NTS · Rev A · 2026-10-26 · mm	**PRELIMINARY**

03

Insulation and lining

Fix battens and fit EPS between them; foam-seal every joint

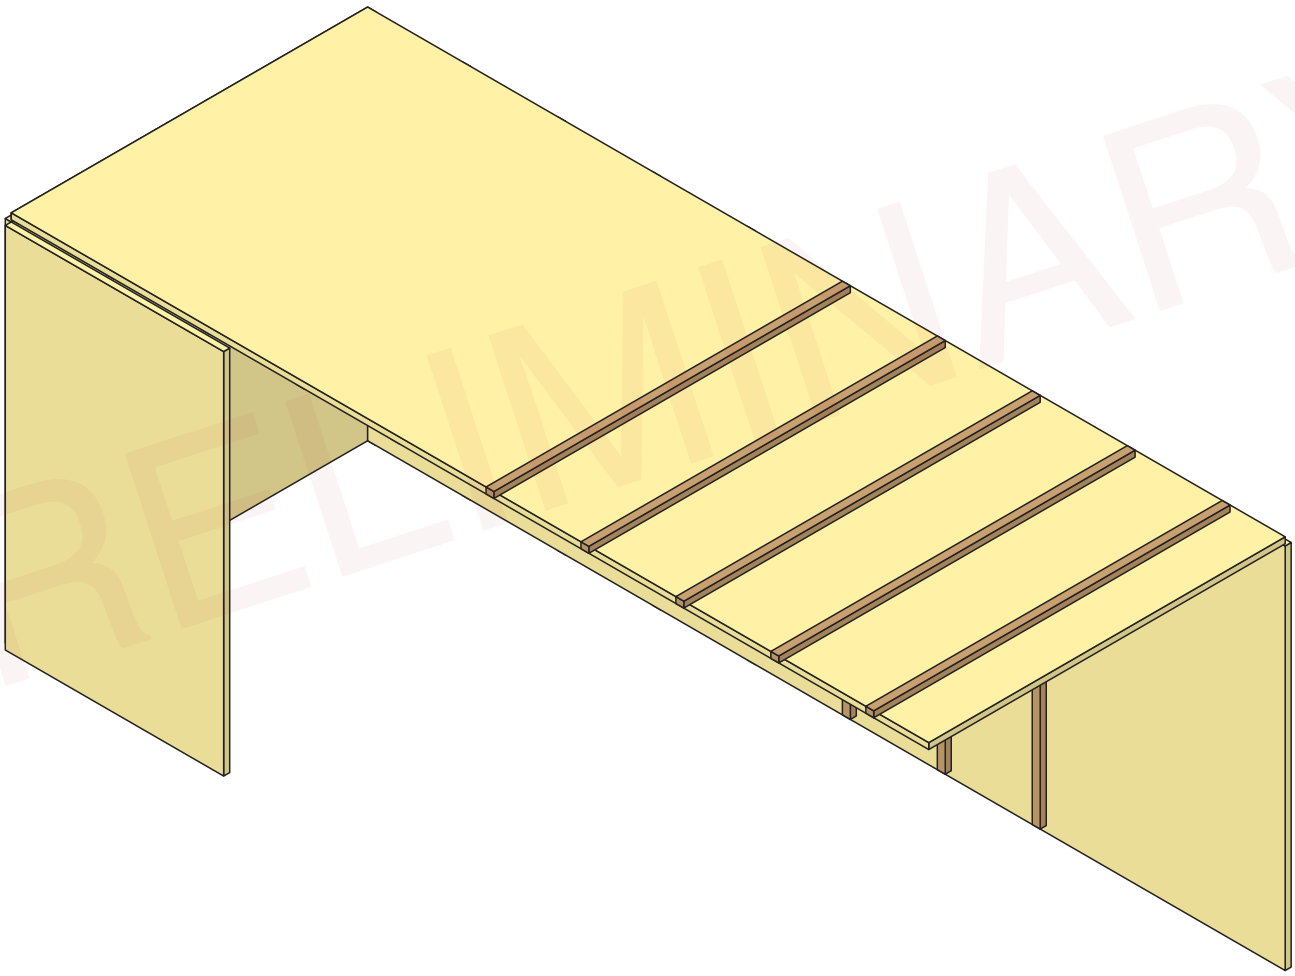

sds

120x L


Farm container studios	farm.databayt.org/docs/studio
Fix battens and fit EPS between them; foam-seal every joint	**AS-03**
Scale NTS · Rev A · 2026-10-26 · mm	**PRELIMINARY**

PRELIMINARY

04

Insulation and lining

Fix the numbered lining panels (cut-outs already in place)

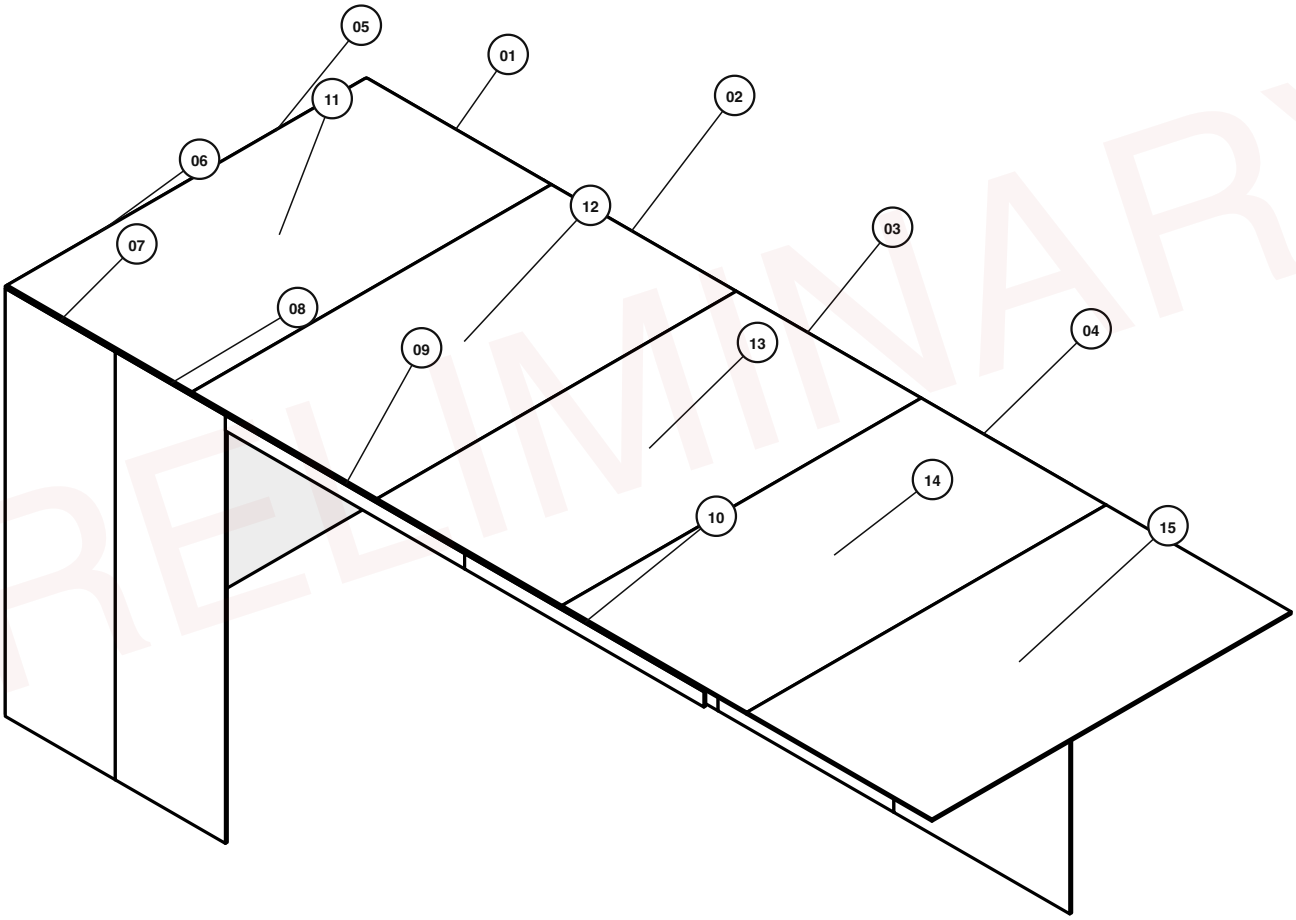

screw

120x F

Farm container studios	farm.databayt.org/docs/studio
Fix the numbered lining panels (cut-outs already in place)	**AS-04**
Scale NTS · Rev A · 2026-10-26 · mm	**PRELIMINARY**

PRELIMINARY

05

Electrical

Services first fix: earth rod, conduits and cables, pipes in the floor



PRELIMINARY


! Licensed electrician and plumber on site.

Farm container studios	farm.databayt.org/docs/studio
Services first fix: earth rod, conduits and cables, pipes in the	**AS-05**
Scale NTS · Rev A · 2026-10-26 · mm	PRELIMINARY

06

Bathroom

Stand the partition frame and fix the living-face skins

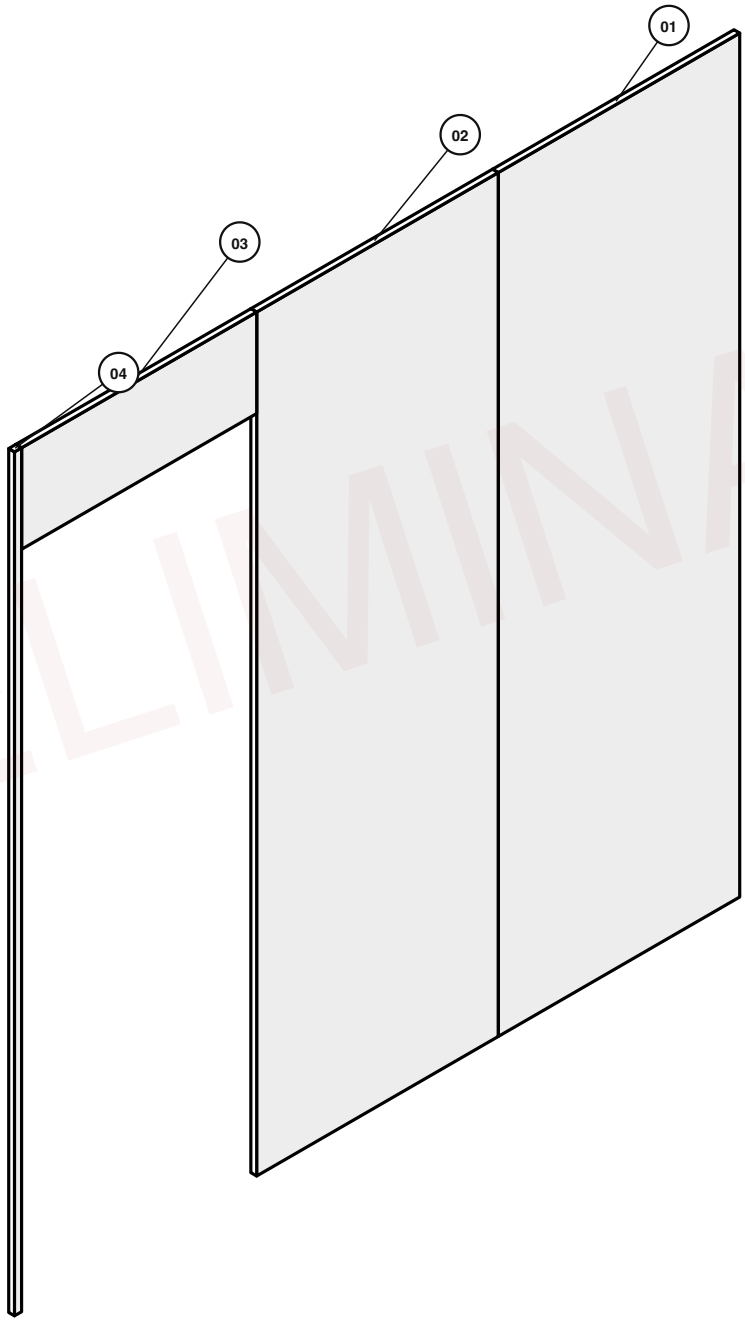

screw

40x F


Farm container studios	farm.databayt.org/docs/studio
Stand the partition frame and fix the living-face skins	**AS-06**
Scale NTS · Rev A · 2026-10-26 · mm	**PRELIMINARY**

PRELIMINARY

07

Bathroom

Fit the door frame and hang the bathroom door

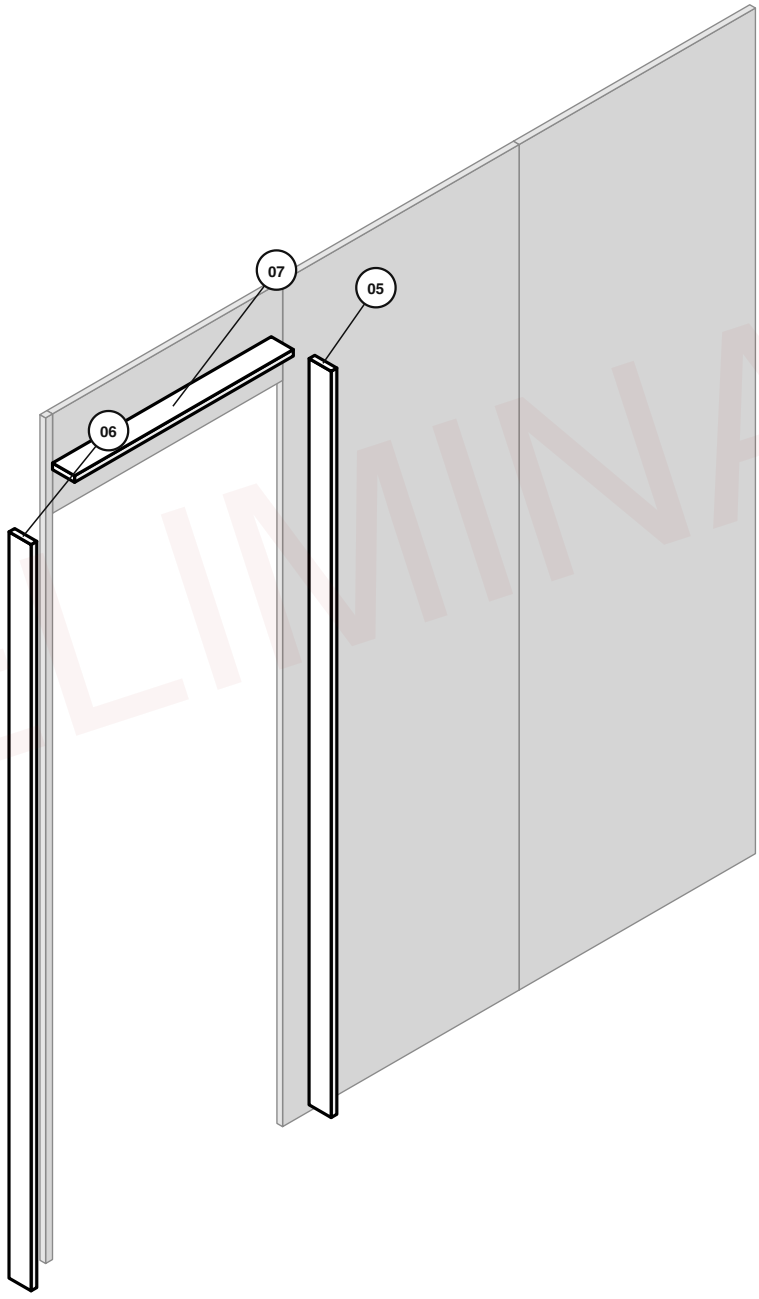

screw

16x F


Farm container studios	farm.databayt.org/docs/studio
Fit the door frame and hang the bathroom door	**AS-07**
Scale NTS · Rev A · 2026-10-26 · mm	**PRELIMINARY**

PRELIMINARY

08

Bathroom

Cement board, membrane and tiles on the wet walls; coved vinyl floor

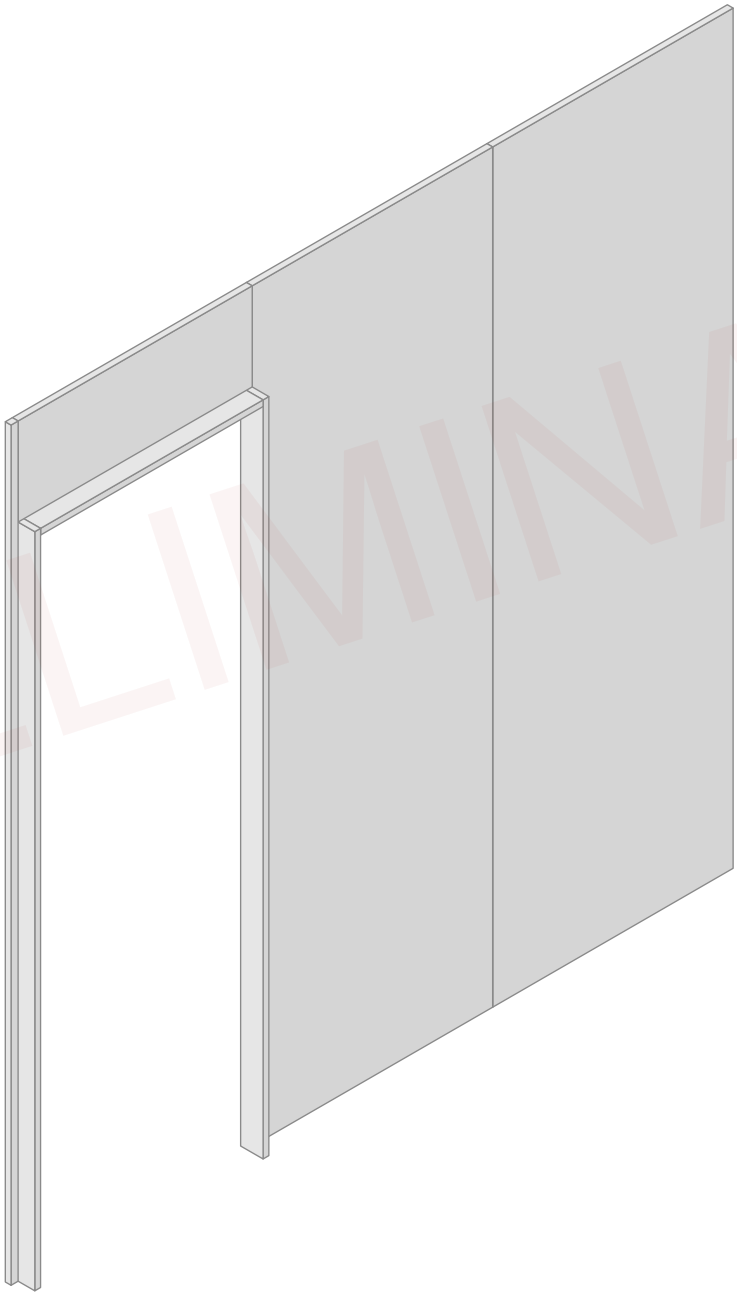


PRELIMINARY

Farm container studios	farm.databayt.org/docs/studio
Cement board, membrane and tiles on the wet walls; coved vinyl	**AS-08**
Scale NTS · Rev A · 2026-10-26 · mm	PRELIMINARY

09

Bathroom

Set the shower tray, ledge and fixed screen

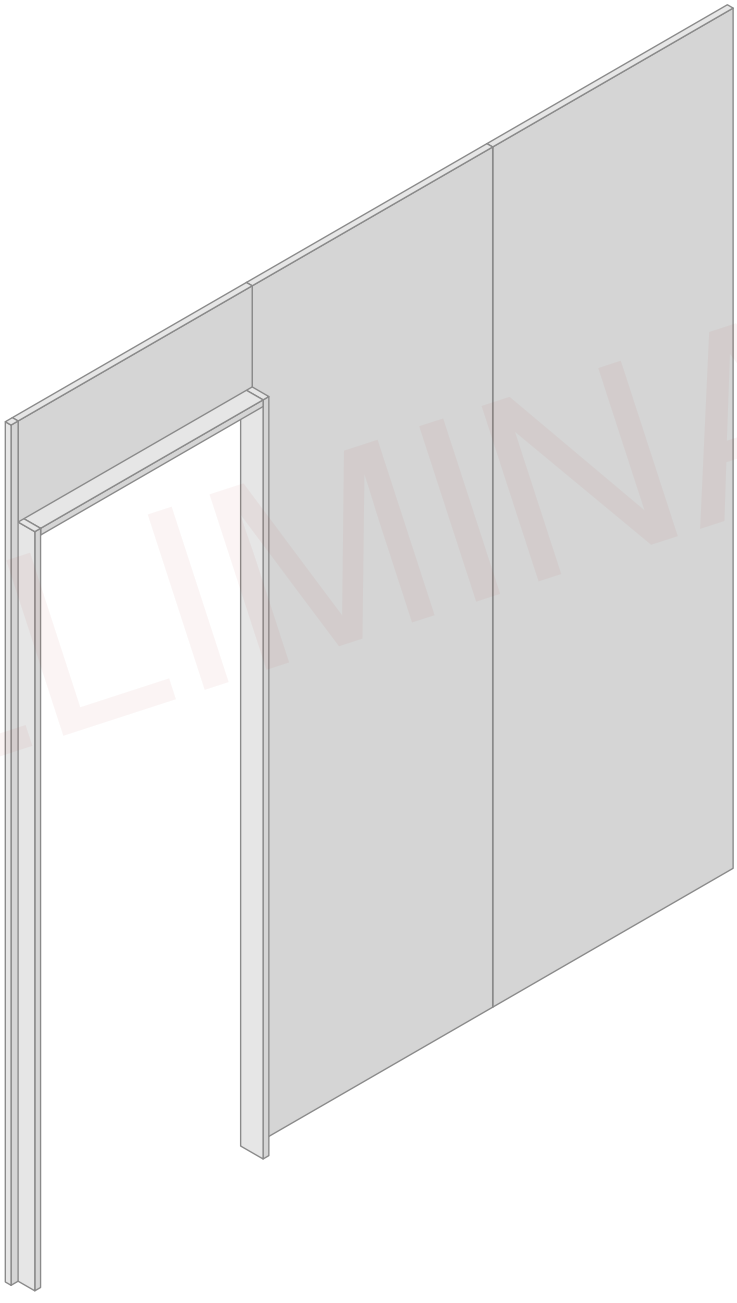


PRELIMINARY

Farm container studios	farm.databayt.org/docs/studio
Set the shower tray, ledge and fixed screen	**AS-09**
Scale NTS · Rev A · 2026-10-26 · mm	PRELIMINARY

10

Bathroom

Hang the WC, basin and mirror cabinet

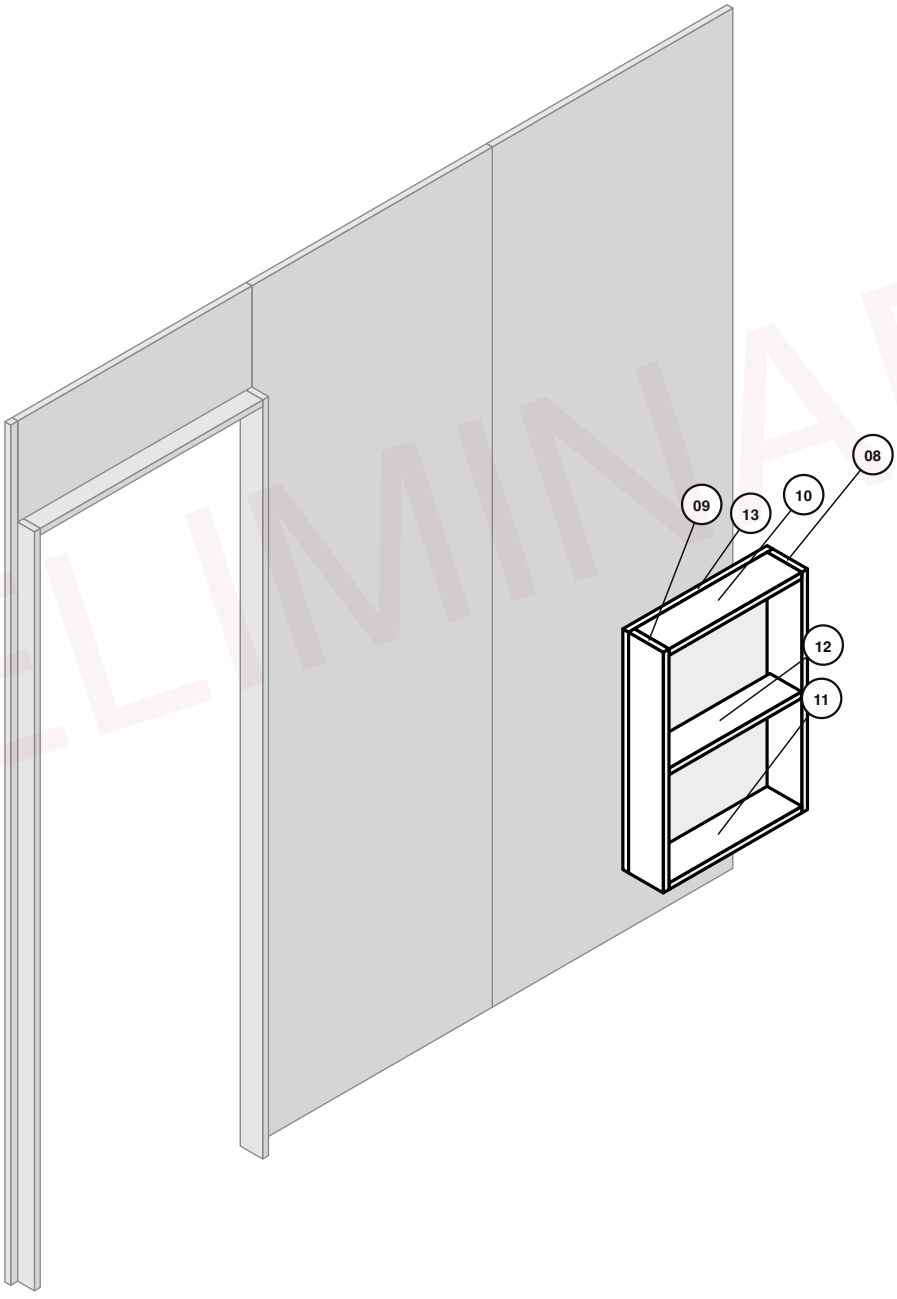

screw

12x F


Farm container studios	farm.databayt.org/docs/studio
Hang the WC, basin and mirror cabinet	**AS-10**
Scale NTS · Rev A · 2026-10-26 · mm	**PRELIMINARY**

PRELIMINARY

11

Kitchen

Assemble the fridge bay, hob base and sink base on their legs

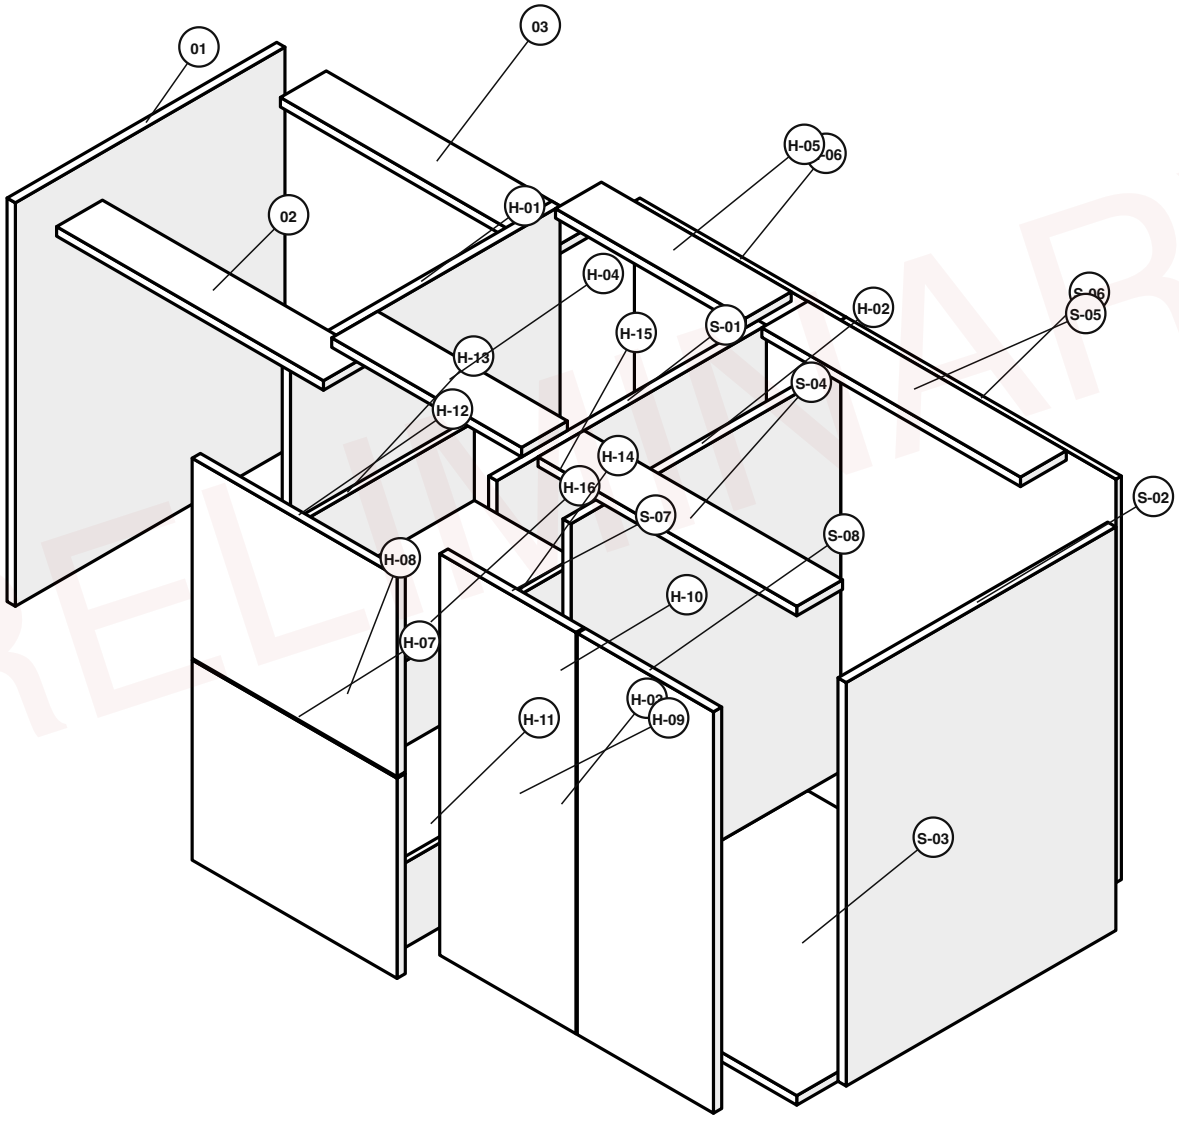


PRELIMINARY

Farm container studios	farm.databayt.org/docs/studio
Assemble the fridge bay, hob base and sink base on their legs	AS-11
Scale NTS · Rev A · 2026-10-26 · mm	PRELIMINARY

12

Kitchen

Assemble the tall unit, fix it to blocking, hang the heater bracket in

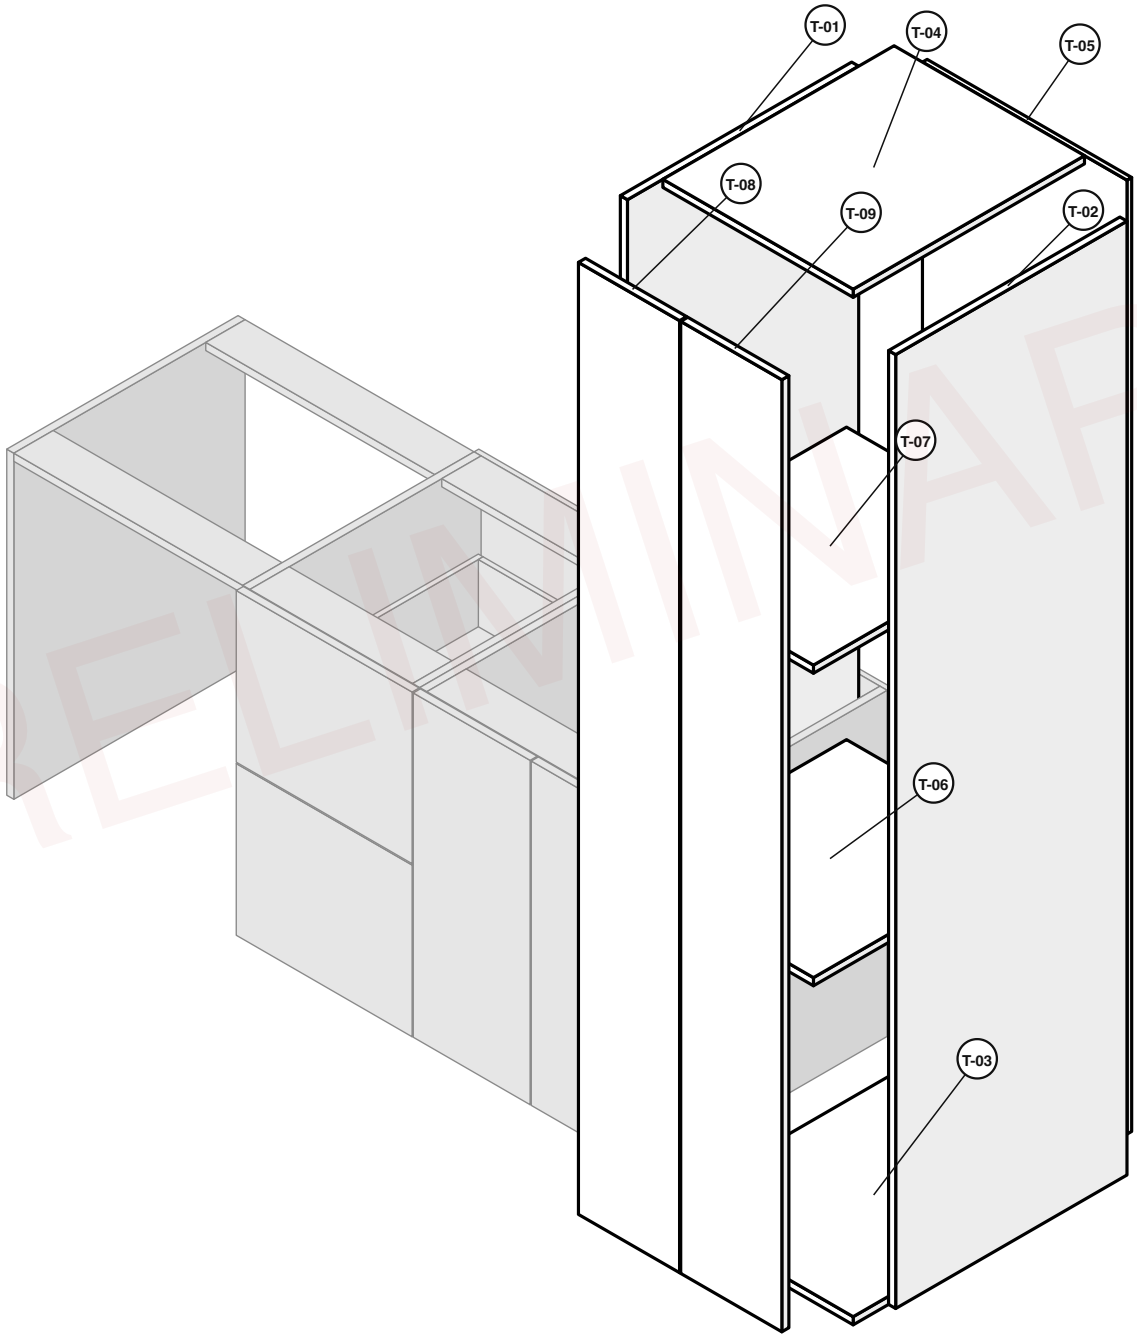

! Tip the tall unit up: two people.


PRELIMINARY

Farm container studios	farm.databayt.org/docs/studio
Assemble the tall unit, fix it to blocking, hang the heater b…	AS-12
Scale NTS · Rev A · 2026-10-26 · mm	PRELIMINARY

13

Kitchen

Scribe and fix the worktop; drop in the sink and hob; plinth

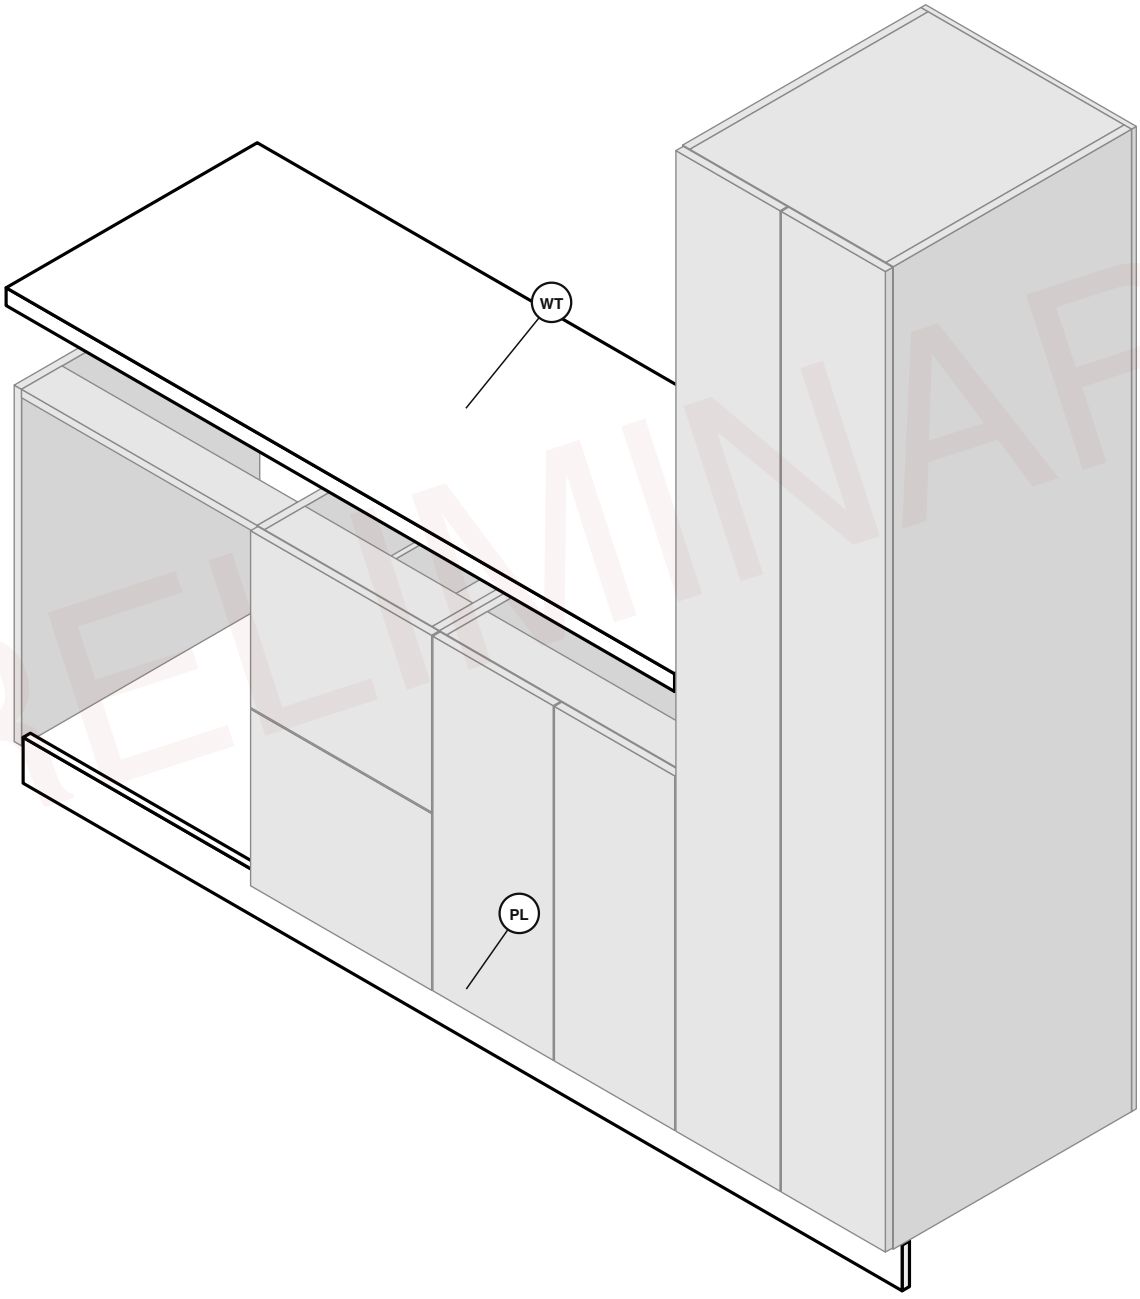

screw
12x F


Farm container studios	farm.databayt.org/docs/studio
Scribe and fix the worktop; drop in the sink and hob; plinth	**AS-13**
Scale NTS · Rev A · 2026-10-26 · mm	**PRELIMINARY**

PRELIMINARY

14

Kitchen

Hang the wall units and the hood shelf on the steel rail

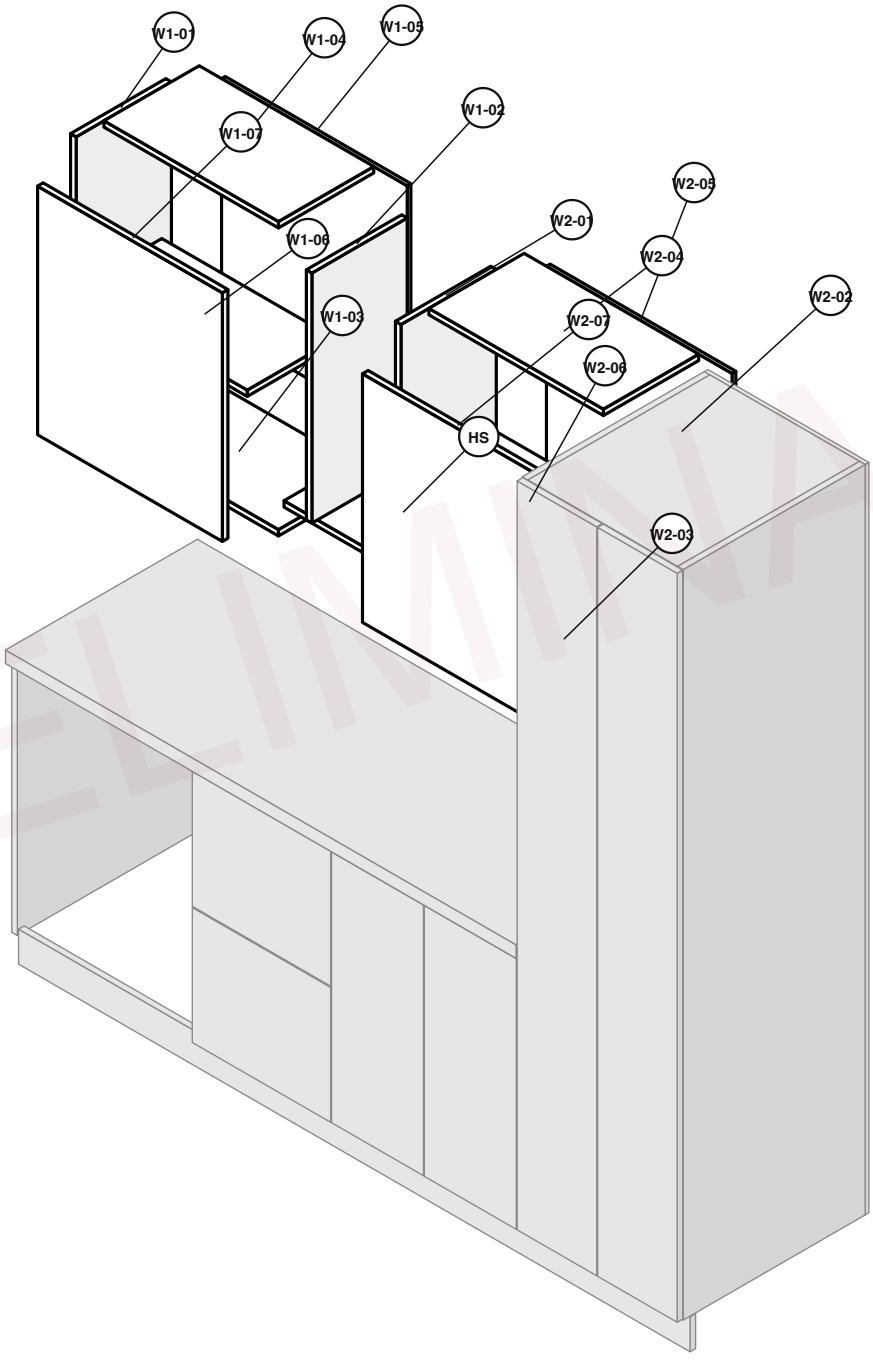

screw


8x F

Farm container studios	farm.databayt.org/docs/studio
Hang the wall units and the hood shelf on the steel rail	**AS-14**
Scale NTS · Rev A · 2026-10-26 · mm	**PRELIMINARY**

PRELIMINARY

15 Bed

Bolt the bed frame, drop in the deck panels, slide in the drawers

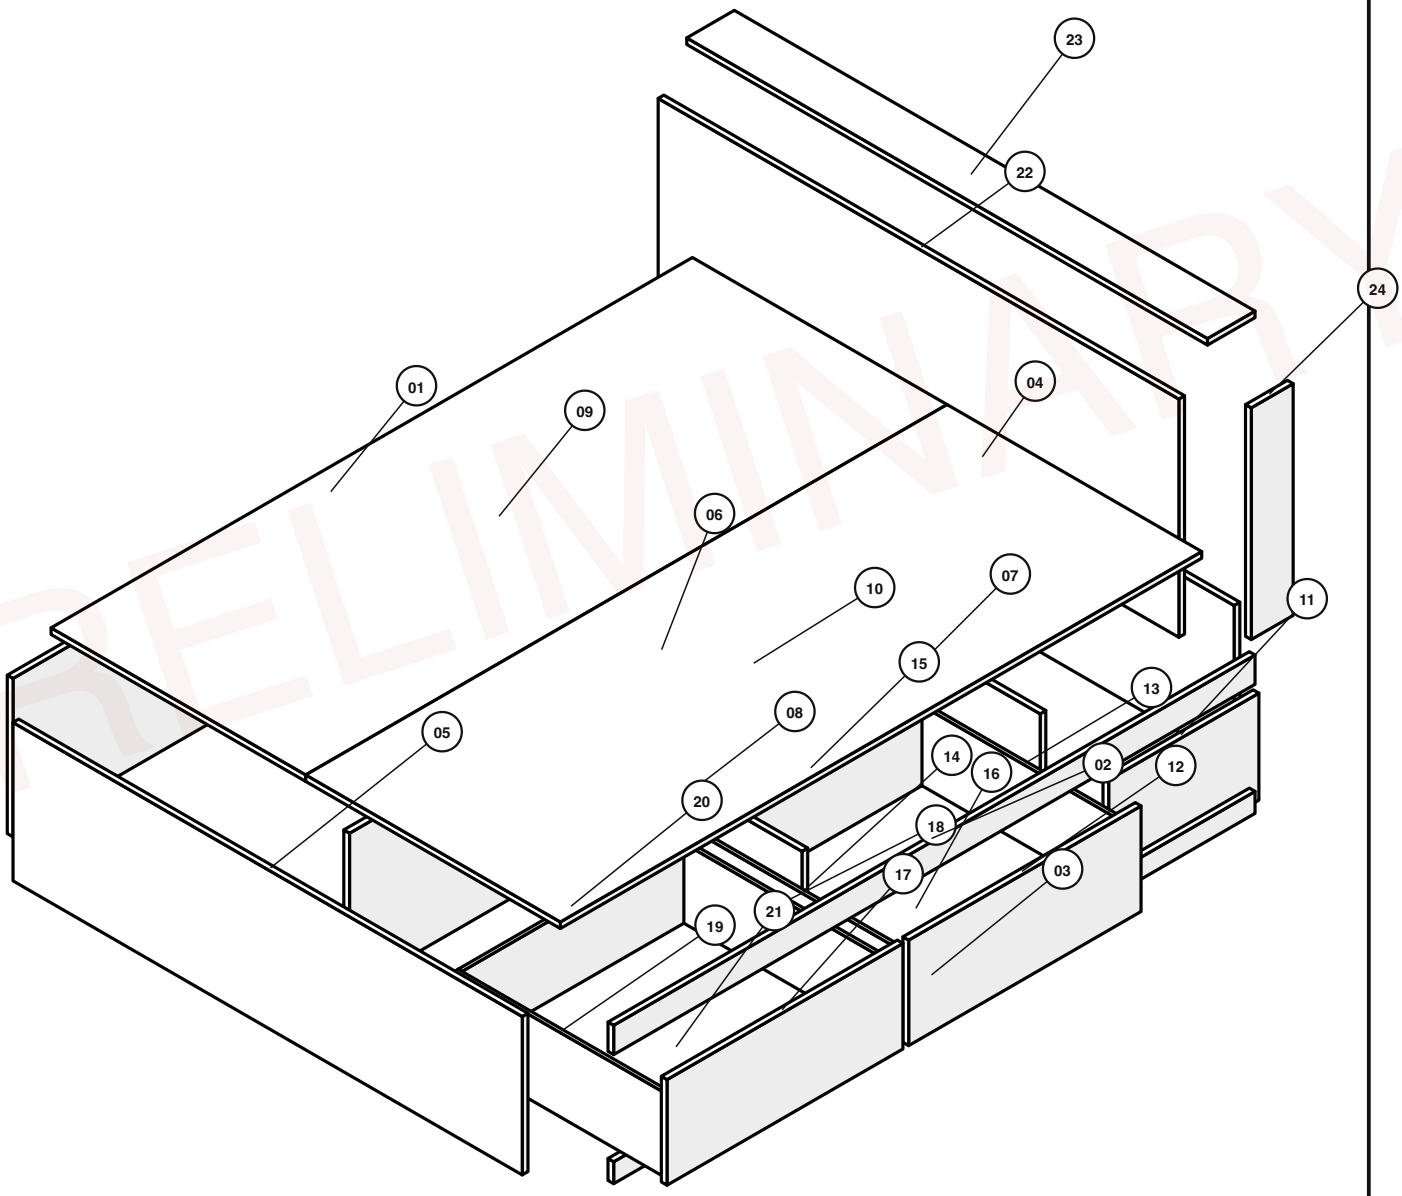

bolt	castor
20x C	**8x K**

Farm container studios farm.databayt.org/docs/studio

Bolt the bed frame, drop in the deck panels, slide in the drawer **AS-15**


Scale NTS · Rev A · 2026-10-26 · mm **PRELIMINARY**

PRELIMINARY

16

Wardrobe

Assemble the wardrobe, fix to blocking, hang the door

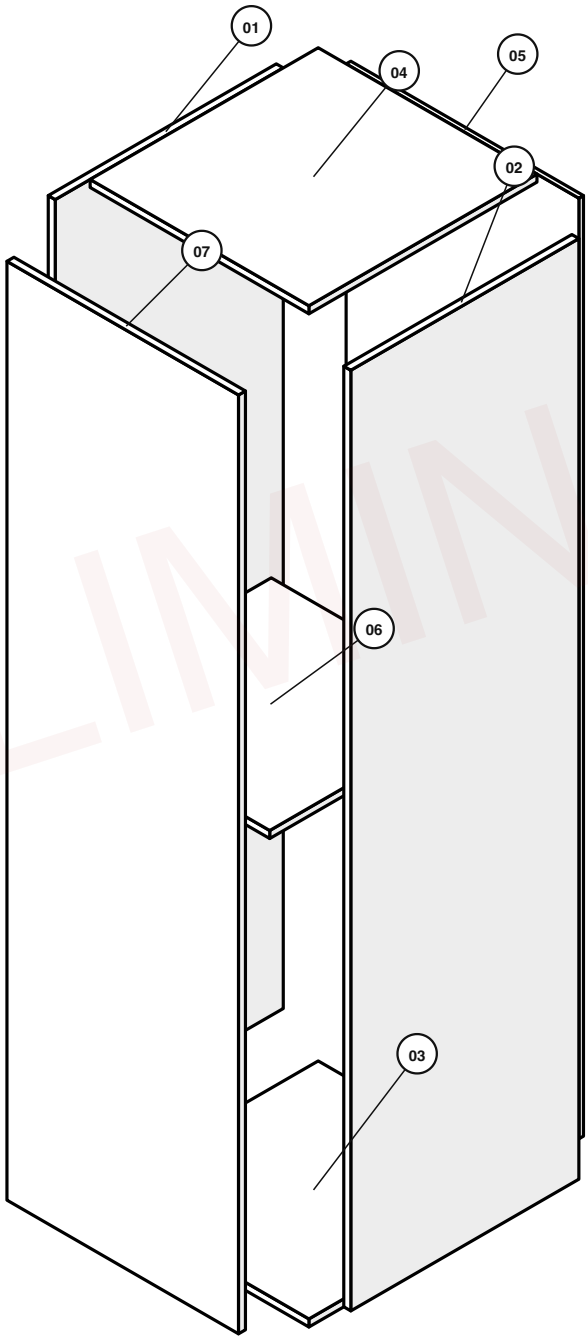

! Tip up: two people.


PRELIMINARY

Farm container studios	farm.databayt.org/docs/studio
Assemble the wardrobe, fix to blocking, hang the door	AS-16
Scale NTS · Rev A · 2026-10-26 · mm	PRELIMINARY

17

Table and stools

Slot together the table and stools

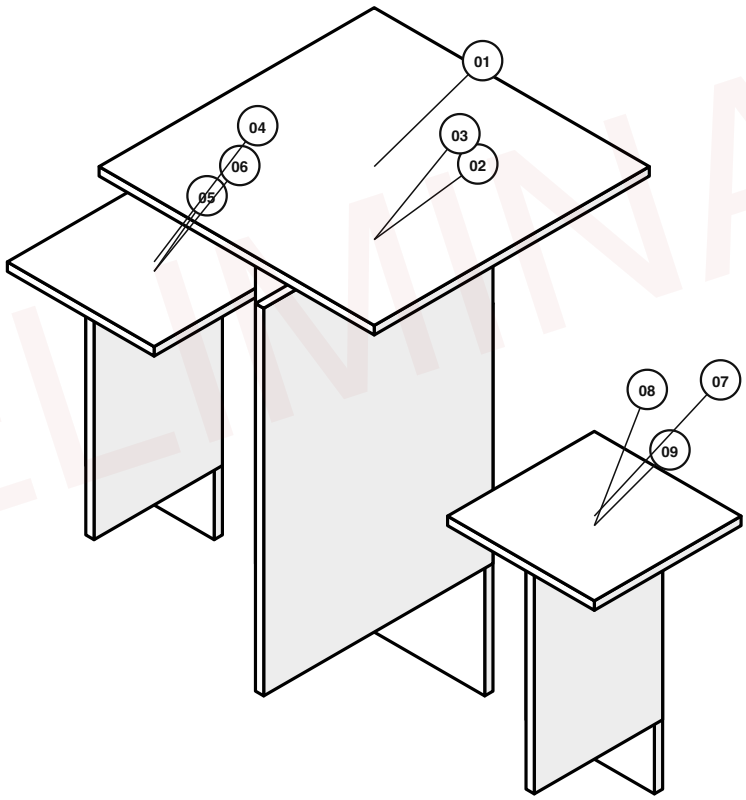


PRELIMINARY

Farm container studios	farm.databayt.org/docs/studio
Slot together the table and stools	**AS-17**
Scale NTS · Rev A · 2026-10-26 · mm	PRELIMINARY

18 Trims

Scribe and pin the trims; caulk and paint

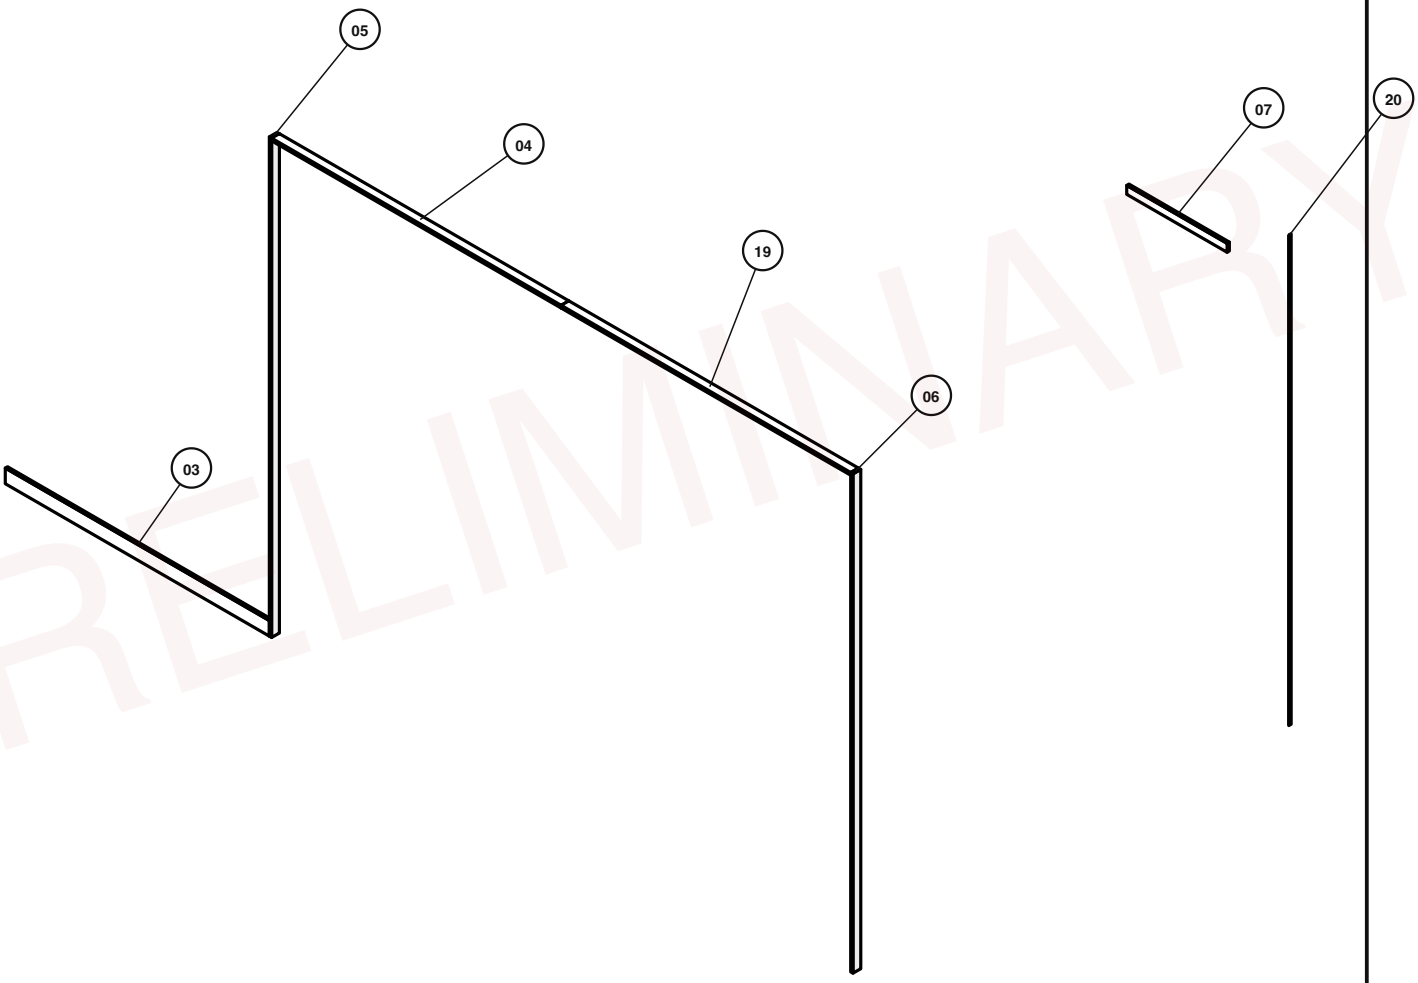

screw

60x F

Farm container studios	farm.databayt.org/docs/studio
Scribe and pin the trims; caulk and paint	**AS-18**
Scale NTS · Rev A · 2026-10-26 · mm	PRELIMINARY

PRELIMINARY

19 Electrical

Second fix: unit board, devices, lights, alarms; test and certify



! Certificate from a RURA class A electrician before power-on.


PRELIMINARY

Farm container studios	farm.databayt.org/docs/studio
Second fix: unit board, devices, lights, alarms; test and certify	AS-19
Scale NTS · Rev A · 2026-10-26 · mm	PRELIMINARY

20

Roof terrace

Lift and bolt the deck beams onto the corner castings; joists

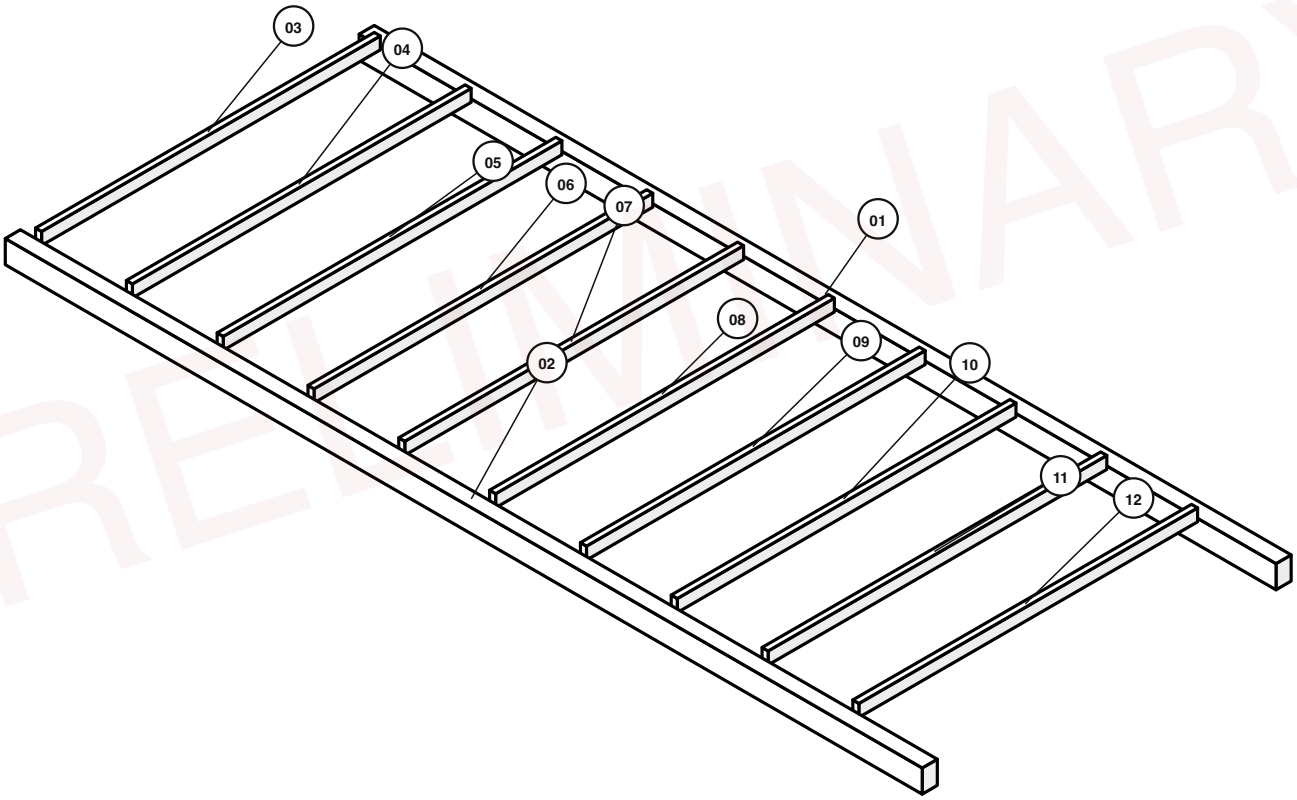


PRELIMINARY

Farm container studios	farm.databayt.org/docs/studio
Lift and bolt the deck beams onto the corner castings; joists	AS-20
Scale NTS · Rev A · 2026-10-26 · mm	PRELIMINARY

21

Roof terrace

Screw down the deck boards (5 mm gaps)

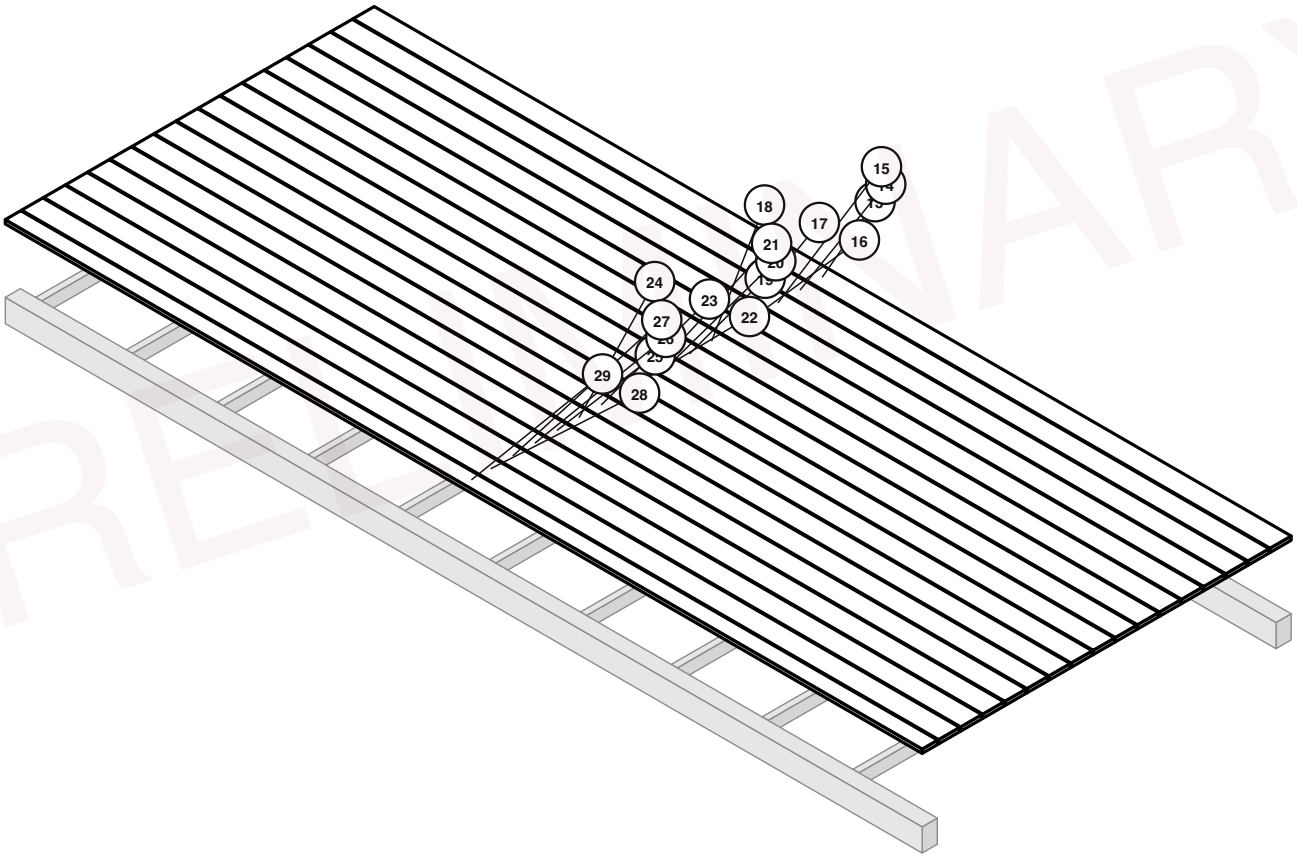


PRELIMINARY

Farm container studios	farm.databayt.org/docs/studio
Screw down the deck boards (5 mm gaps)	**AS-21**
Scale NTS · Rev A · 2026-10-26 · mm	PRELIMINARY

22

Roof terrace

Bolt on the guardrail panels

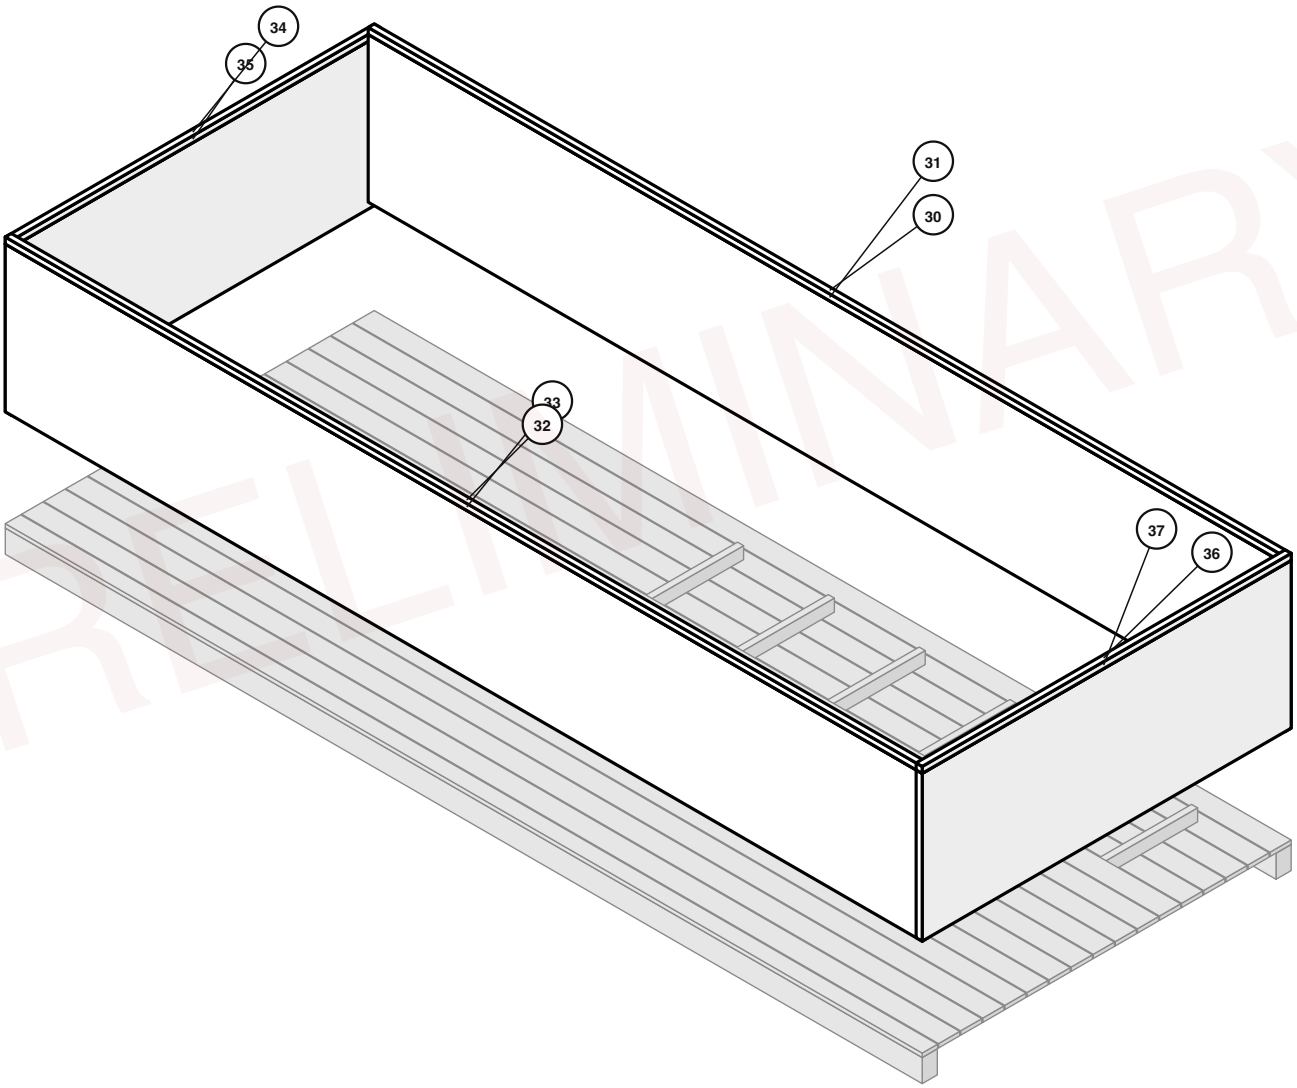


PRELIMINARY

Farm container studios	farm.databayt.org/docs/studio
Bolt on the guardrail panels	**AS-22**
Scale NTS · Rev A · 2026-10-26 · mm	PRELIMINARY

23

Roof terrace

Stand the canopy posts; rafters; polycarbonate; gutter

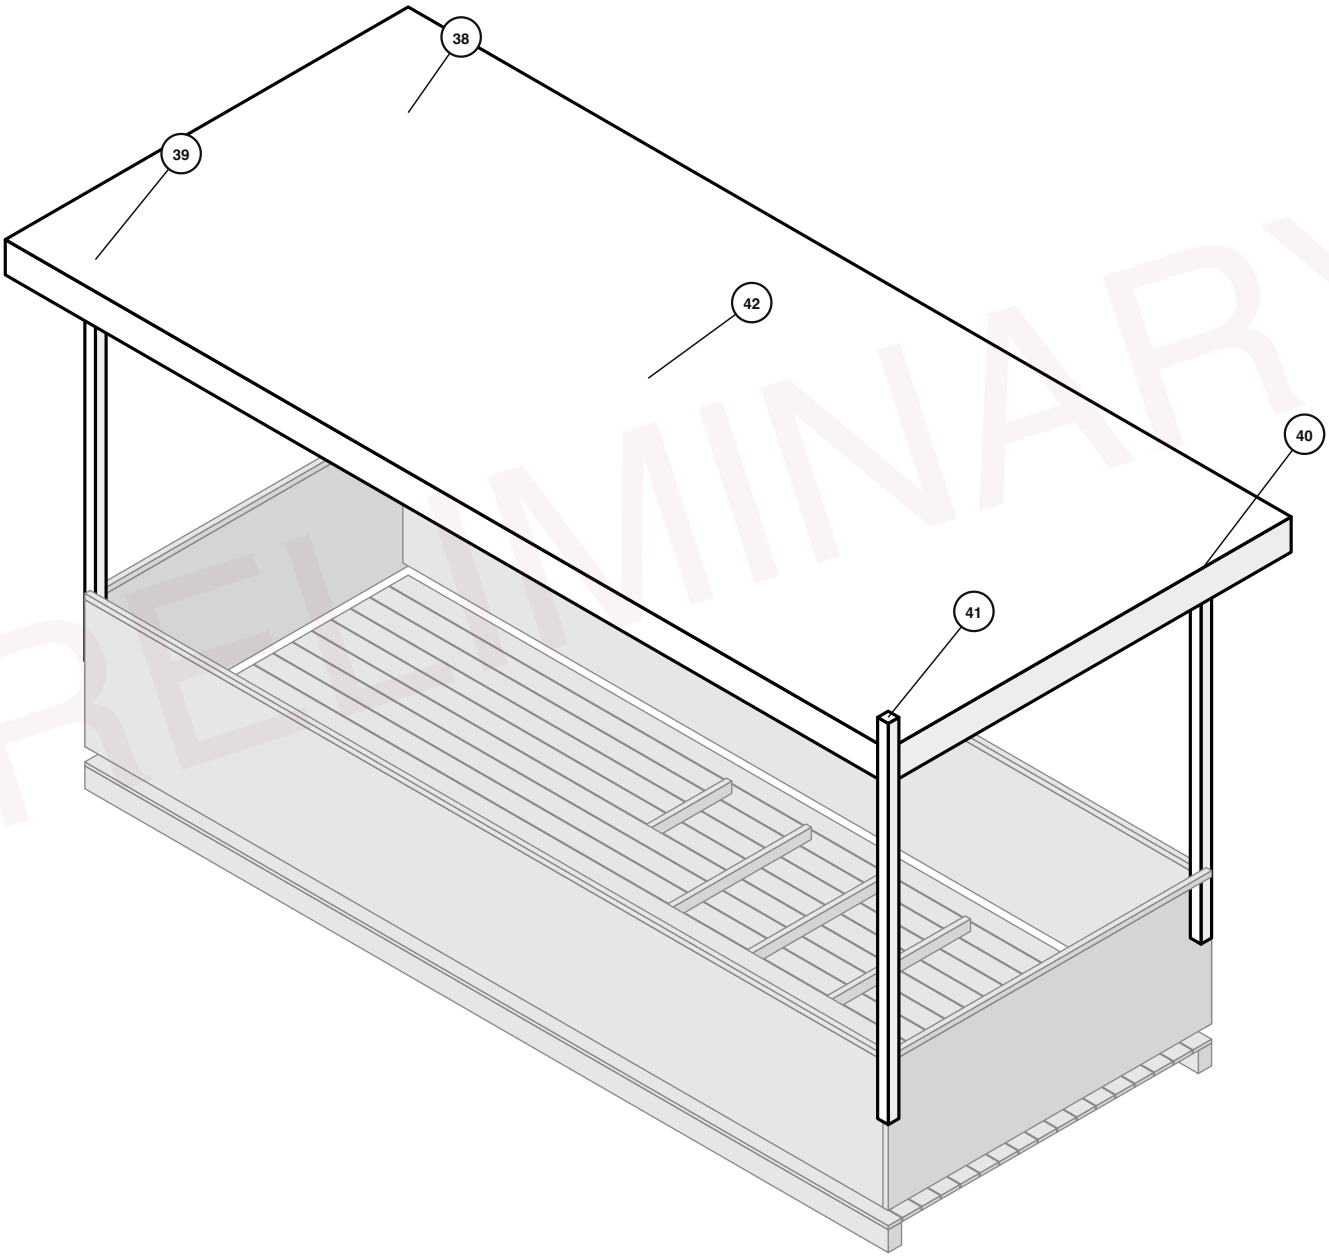


PRELIMINARY

Farm container studios	farm.databayt.org/docs/studio
Stand the canopy posts; rafters; polycarbonate; gutter	**AS-23**
Scale NTS · Rev A · 2026-10-26 · mm	PRELIMINARY

24

Roof terrace

Veranda posts, ledger and polycarbonate over the front deck

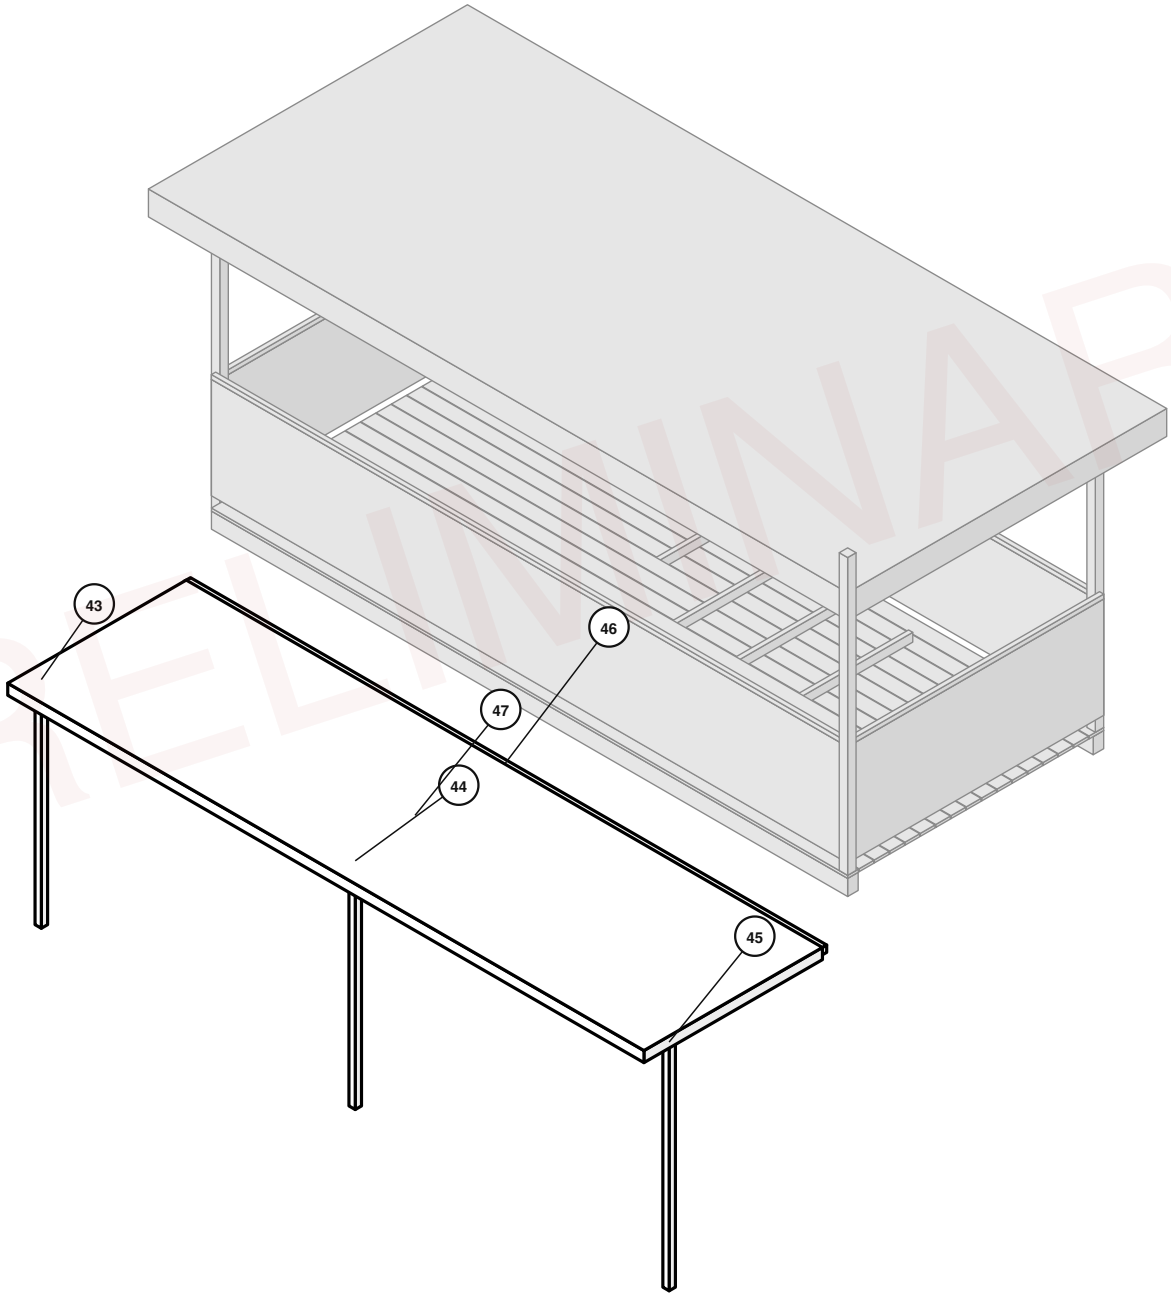


PRELIMINARY

Farm container studios	farm.databayt.org/docs/studio
Veranda posts, ledger and polycarbonate over the front deck	AS-24
Scale NTS · Rev A · 2026-10-26 · mm	PRELIMINARY

25

Roof terrace

Set the stair footings; bolt the two flights and the landing

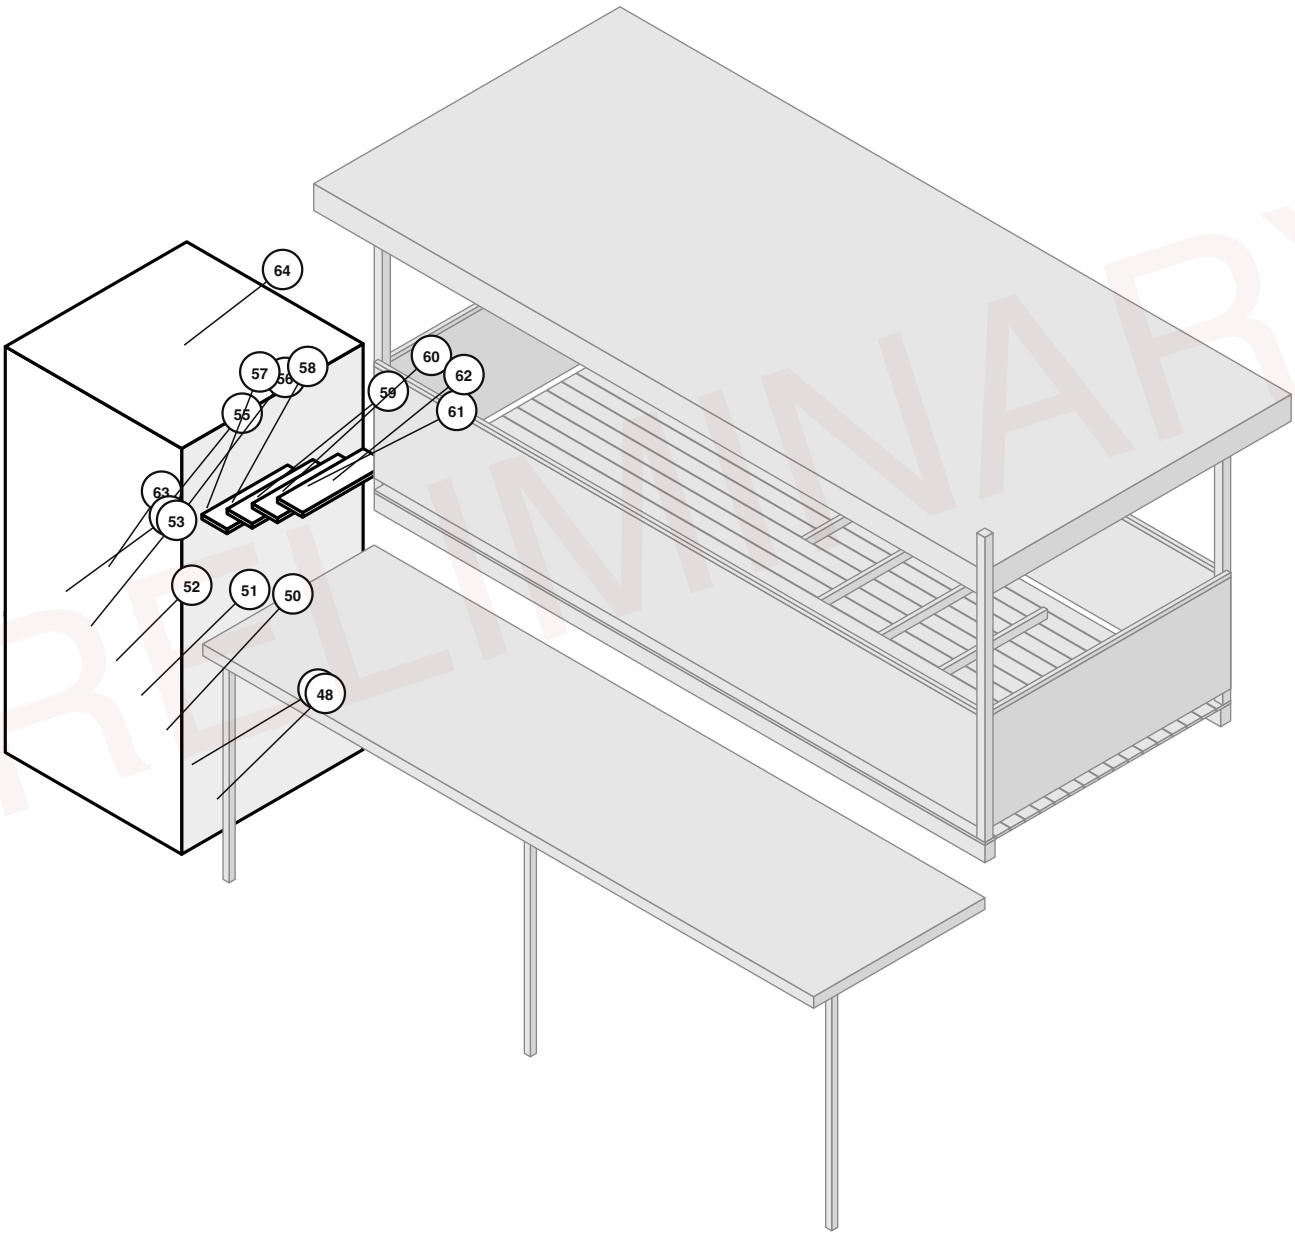


PRELIMINARY

Farm container studios	farm.databayt.org/docs/studio
Set the stair footings; bolt the two flights and the landing	**AS-25**
Scale NTS · Rev A · 2026-10-26 · mm	PRELIMINARY

26

Roof terrace

Place the chairs and the side table

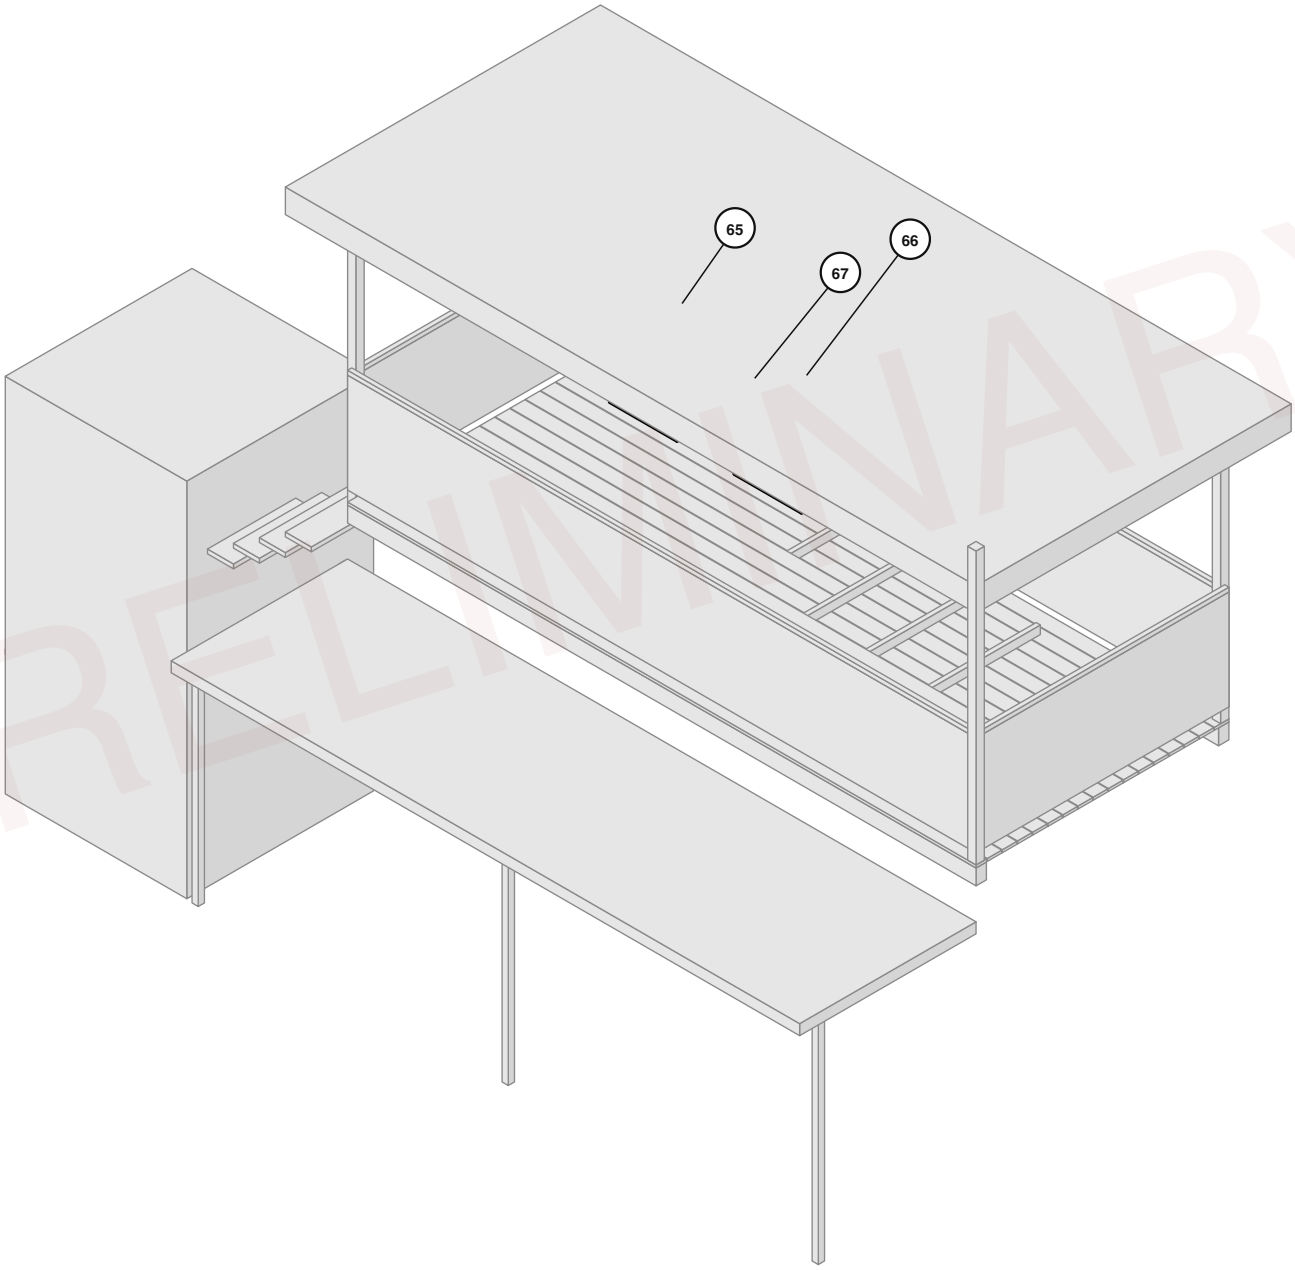


PRELIMINARY

Farm container studios	farm.databayt.org/docs/studio
Place the chairs and the side table	**AS-26**
Scale NTS · Rev A · 2026-10-26 · mm	PRELIMINARY

27

Roof terrace

Bond the steelwork to earth; engineer's inspection before guest use

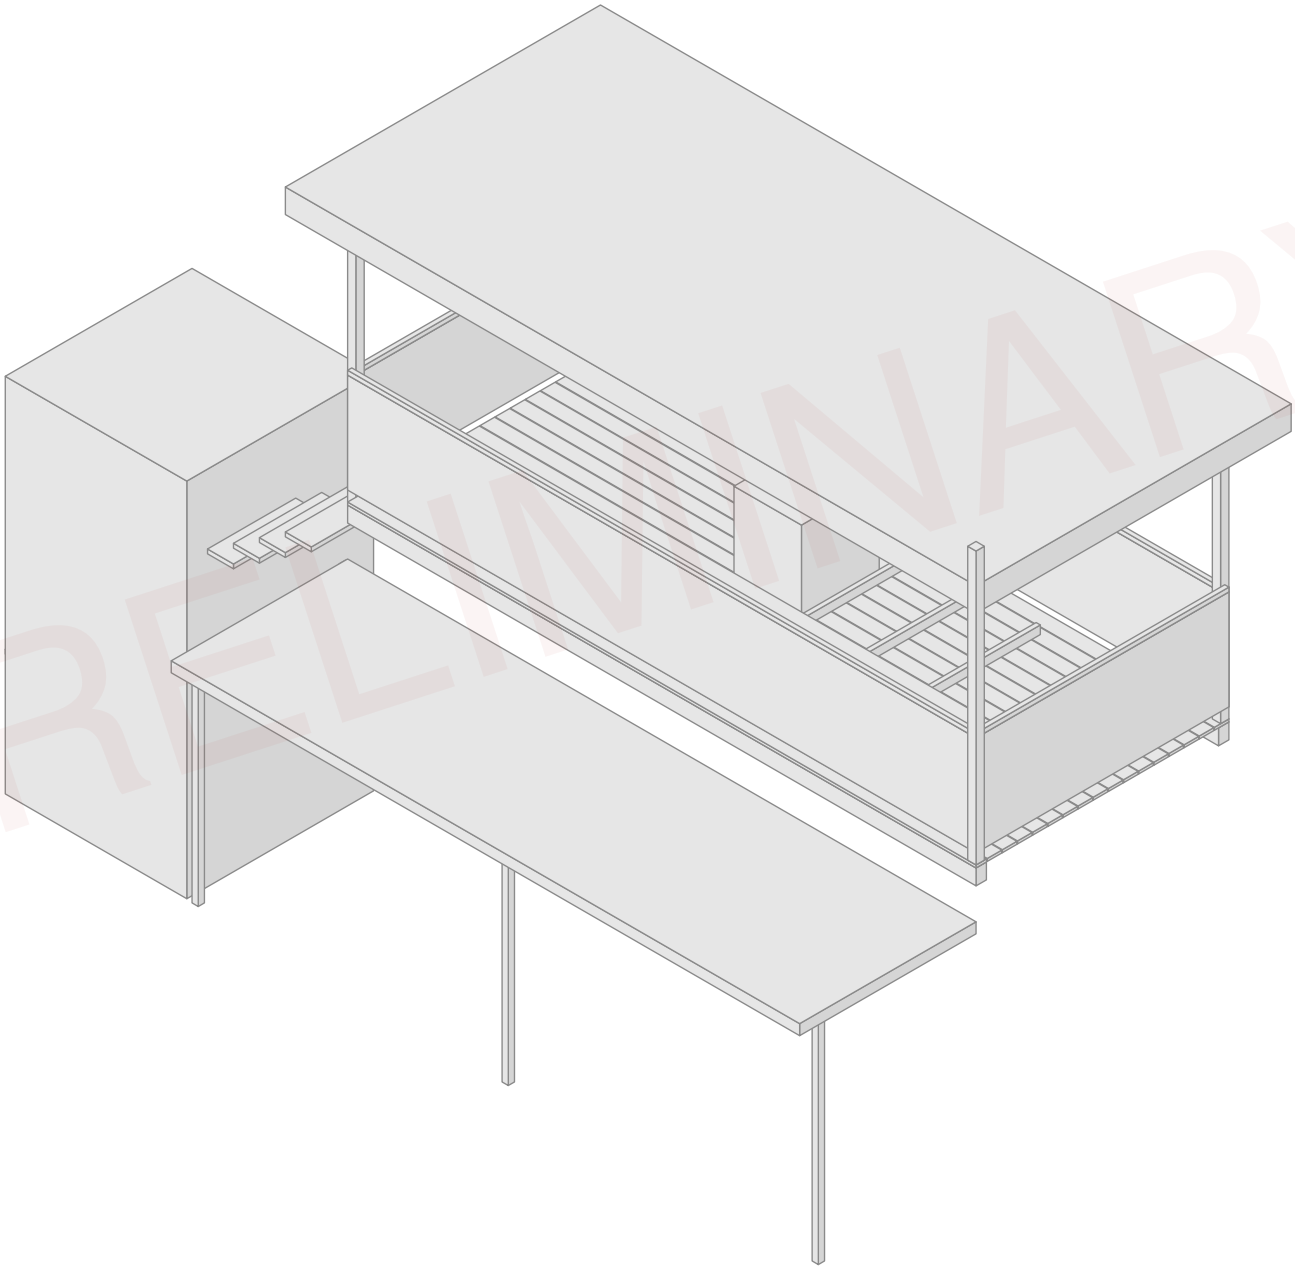

PRELIMINARY

Farm container studios	farm.databayt.org/docs/studio
Bond the steelwork to earth; engineer's inspection before guest	AS-27
Scale NTS · Rev A · 2026-10-26 · mm	PRELIMINARY